
DIAGRAMA DE PLANTA DE TRATAMIENTO DE AGUAS RESIDUALES (PTAR) S&U

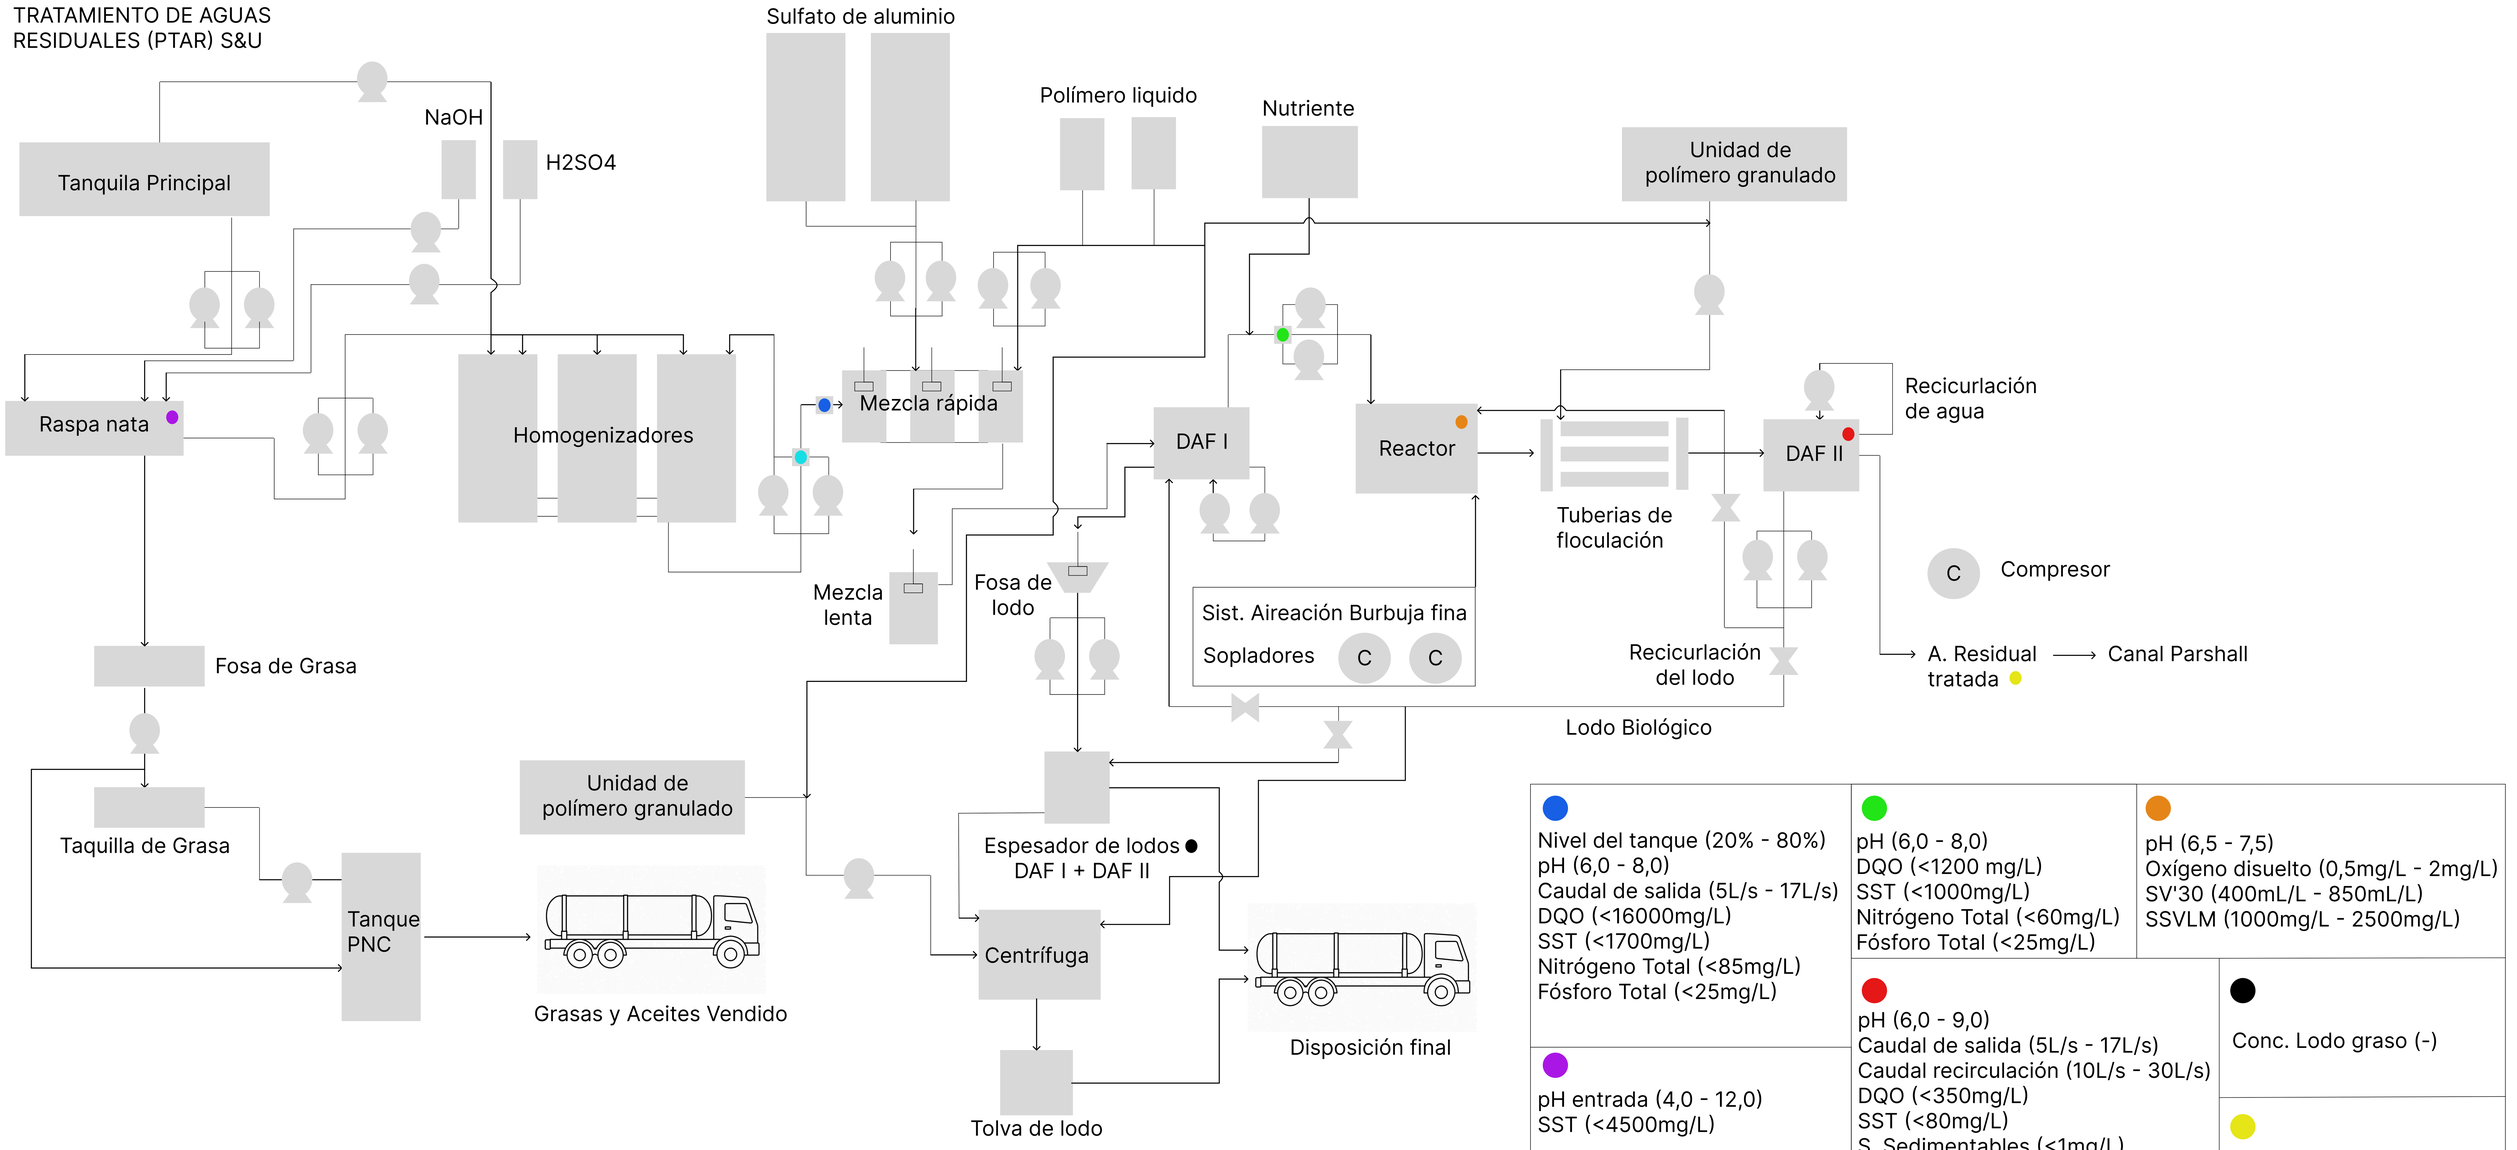

- Nivel del tanque (20% - 80%)
  pH (6,0 - 8,0)
  Caudal de salida (5L/s - 17L/s)
  DQO (<16000mg/L)
  SST (<1700mg/L)
  Nitrógeno Total (<85mg/L)
  Fósforo Total (<25mg/L)
- pH entrada (4,0 - 12,0)
  SST (<4500mg/L)
- Lecturas del homogenizador (-)
- pH (6,0 - 8,0)
  DQO (<1200 mg/L)
  SST (<1000mg/L)
  Nitrógeno Total (<60mg/L)
  Fósforo Total (<25mg/L)
- pH (6,0 - 9,0)
  Caudal de salida (5L/s - 17L/s)
  Caudal recirculación (10L/s - 30L/s)
  DQO (<350mg/L)
  SST (<80mg/L)
  S. Sedimentables (<1mg/L)
  Nitrógeno total (<10mg/L)
  Fósforo Total (<1mg/L)
  Lecturas del DAF II (-)
- pH (6,5 - 7,5)
  Oxígeno disuelto (0,5mg/L - 2mg/L)
  SV'30 (400mL/L - 850mL/L)
  SSVLM (1000mg/L - 2500mg/L)
- Conc. Lodo graso (-)
- FT-Canal Parshall (-)